

TỔNG CỤC HẬU CẦN
CỤC DOANH TRẠI

THIỆT KẾ MẪU
GIƯỜNG SẮT CHIẾN SĨ 2 TẦNG

KÝ HIỆU GCS 2T-Sa-2016-TCHC

(Ban hành kèm theo Quyết định số 242/QĐ-HC ngày 10/3/2016 của Chủ nhiệm Tổng cục Hậu cần)

Tháng 01/2016



Thiếu tướng Nguyễn Văn Tươi

Chủ trì:

[Signature]

Đại tá Nguyễn Quang Bình

Kiểm tra:

[Signature]

Thiếu tá Phạm Minh Thắng

Thiết kế:

[Signature]

Trung tá Nguyễn Xuân Vĩnh

THIẾT KẾ MẪU DOANH CỤ
GIƯỜNG SẮT CHIẾN SĨ 2 TẦNG

Tên bản vẽ:

BẢN LẬP


Ký hiệu:

GCS 2T-Sa-2016-TCHC

Hoàn thành: 01/2016

Bản vẽ số:
01/08

Tỷ lệ: 1/100

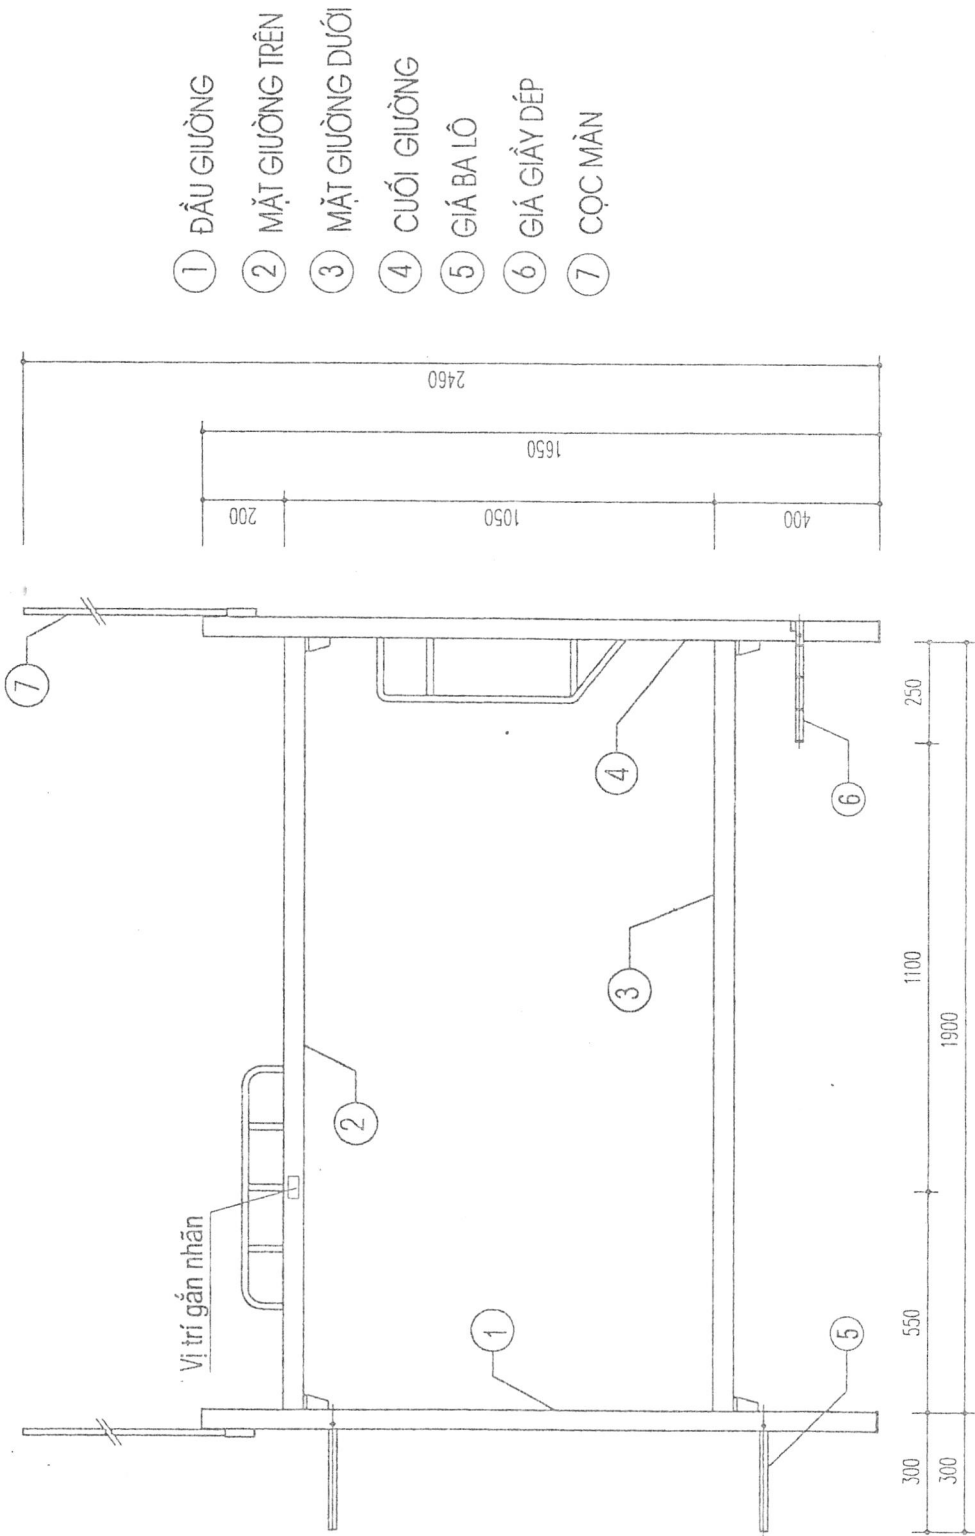


- ① ĐẦU GIƯỜNG
- ② MẶT GIƯỜNG TRÊN
- ③ MẶT GIƯỜNG DƯỚI
- ④ CỐI GIƯỜNG
- ⑤ GIÁ BA LÔ
- ⑥ GIÁ GIẤY DÉP
- ⑦ CỌC MÀN

- Giường sắt 2 tầng được chế tạo từ thép CT38. TCVN 1765-75; lắp ghép từ 4 bộ phận: Đầu giường, cuối giường, mặt giường trên, mặt giường dưới. Liên kết giữa các bộ phận trên bằng các ngàm nối.
- Sơn tĩnh điện toàn bộ màu xanh (theo mẫu)
- Mỗi giường có 2 phần nằm làm bằng gỗ thông.

**TỔNG CỤC HẬU CẦN
CỤC DOANH TRẠI**

CỤC TRƯỞNG

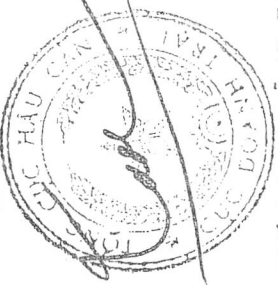

Thiếu tướng Nguyễn Văn Tươi

Chủ trì:

Đại tá Nguyễn Quang Bình

Kiểm tra:

Thiếu tá Phạm Minh Thắng

Thiết kế:

Trung tá Nguyễn Xuân Vinh

THIẾT KẾ MẪU DOANH CỤ
GIƯỜNG SẮT CHIẾN SĨ 2 TẦNG

Tên bản vẽ:

CÁC BỘ PHẬN, CHỈ TIẾT ĐẦU GIƯỜNG

Ký hiệu:

GCS 2T-Sa-2016-TCHC


Hoàn thành: 01/2016

Bản vẽ số:


• Tỷ lệ: 100

02/08


MÓC MÀN

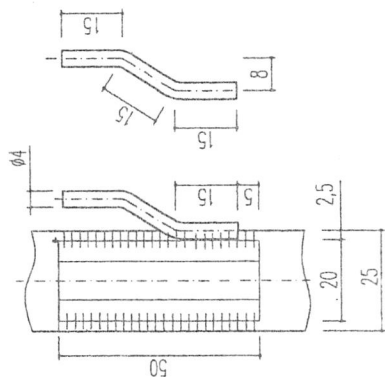

五

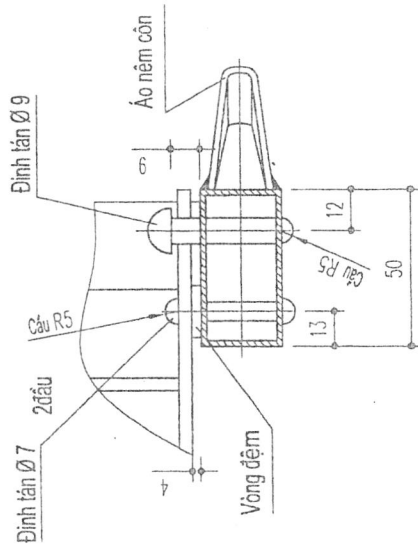


- Liên kết các chi tiết với nhau bằng hàn MIG có khí bảo vệ CO₂.
- Sửa ba vĩa, cạnh sắc.
- Sơn tĩnh điện màu xanh (theo mẫu)

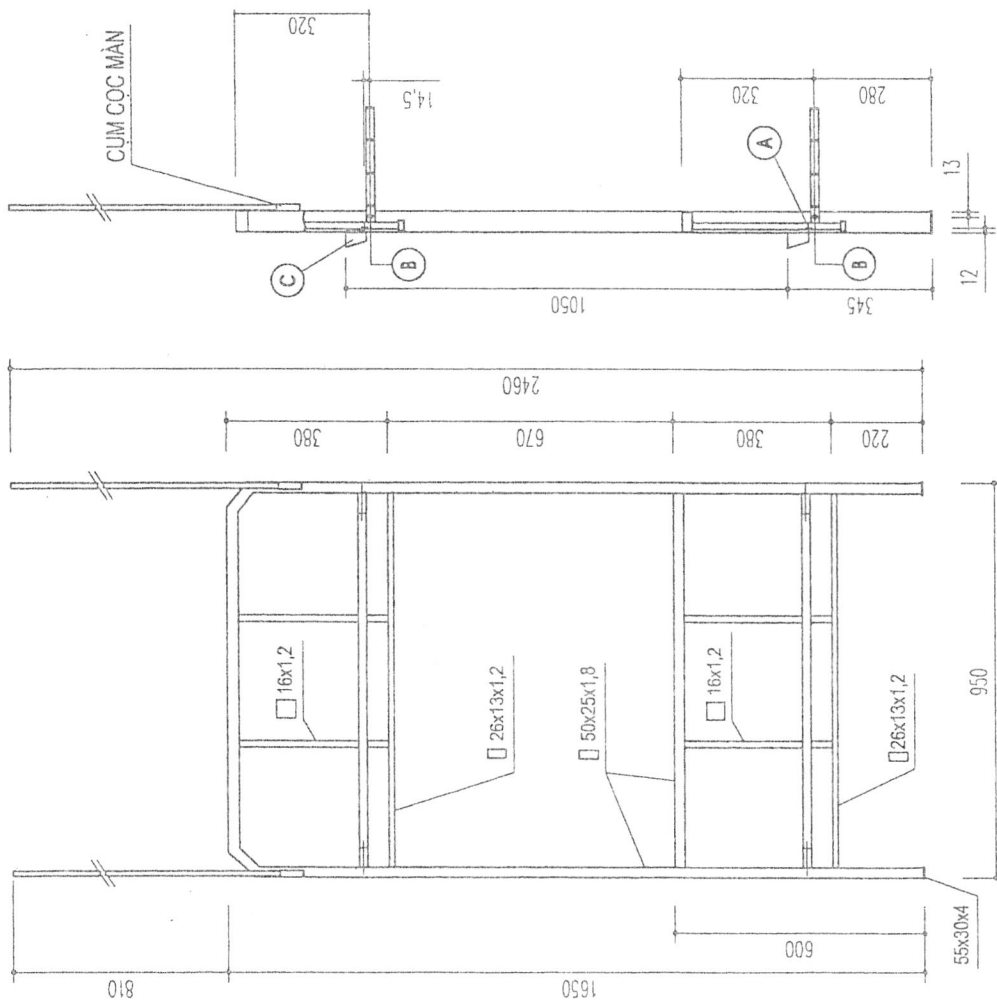

ĐINH TÁN Ø 9

GAH-TAN 97

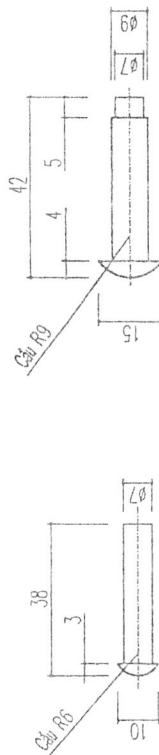

TỔNG CỤC HẬU CẦN
CỤC DOANH TRẠI

CỤC TRƯỞNG



Thiếu tướng Nguyễn Văn Tươi

Chủ trì:

[Signature]

Đại tá Nguyễn Quang Bình

Kiểm tra:

[Signature]

Thiếu tá Phạm Minh Thắng

Thiết kế:

[Signature]

Trung tá Nguyễn Xuân Vinh

THIẾT KẾ MẪU DOANH CỤ
GIƯỜNG SẮT CHIẾN SĨ 2 TẦNG

Tên bản vẽ:

CUỐI GIƯỜNG

Ký hiệu:


GCS 2T-Sa-2016-TCHC

Hoàn thành: 01/2016


Bản vẽ số:

Tỷ lệ: 4/100

03/08

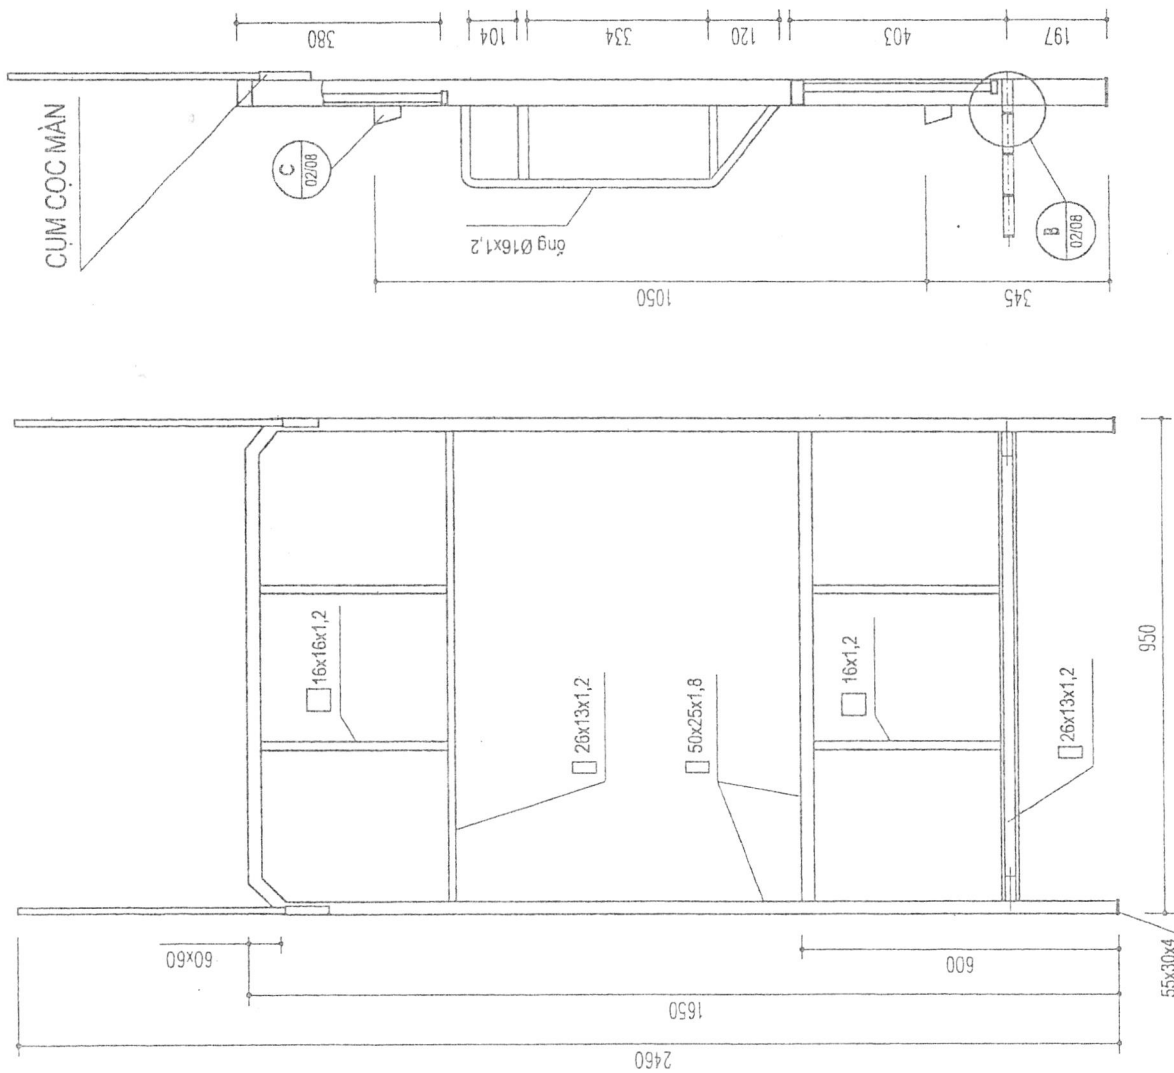


CHI TIẾT THANG LEO

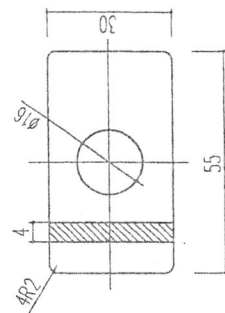

ĐÉ CHÂN GIƯỜNG

- Liên kết các chi tiết với nhau bằng hàn MIG có khí bảo vệ CO₂.
- Sửa ba vĩa, cạnh sắc.
- Sơn tĩnh điện màu xanh (theo mẫu).

CỤC TRƯỞNG

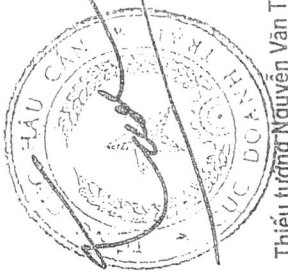

Thiếu tướng Nguyễn Văn Tươi

Chủ trì:

[Signature]

Đại tá Nguyễn Quang Bình

Kiểm tra:

[Signature]

Thiếu tá Phạm Minh Thắng

Thiết kế:

[Signature]

Trung tá Nguyễn Xuân Vinh

THIẾT KẾ MẪU DOANH CỤ
GIƯỜNG SẮT CHIẾN SĨ 2 TẦNG

Tên bản vẽ:

PHẢN NẪM

Ký hiệu:



GCS 2T-Sa-2016-TCHC

Hoàn thành: 01/2016

Bản vẽ số:


Tỷ lệ: 1/100

08/08

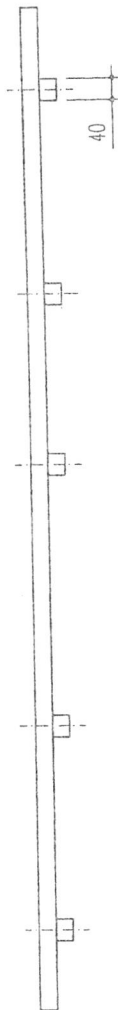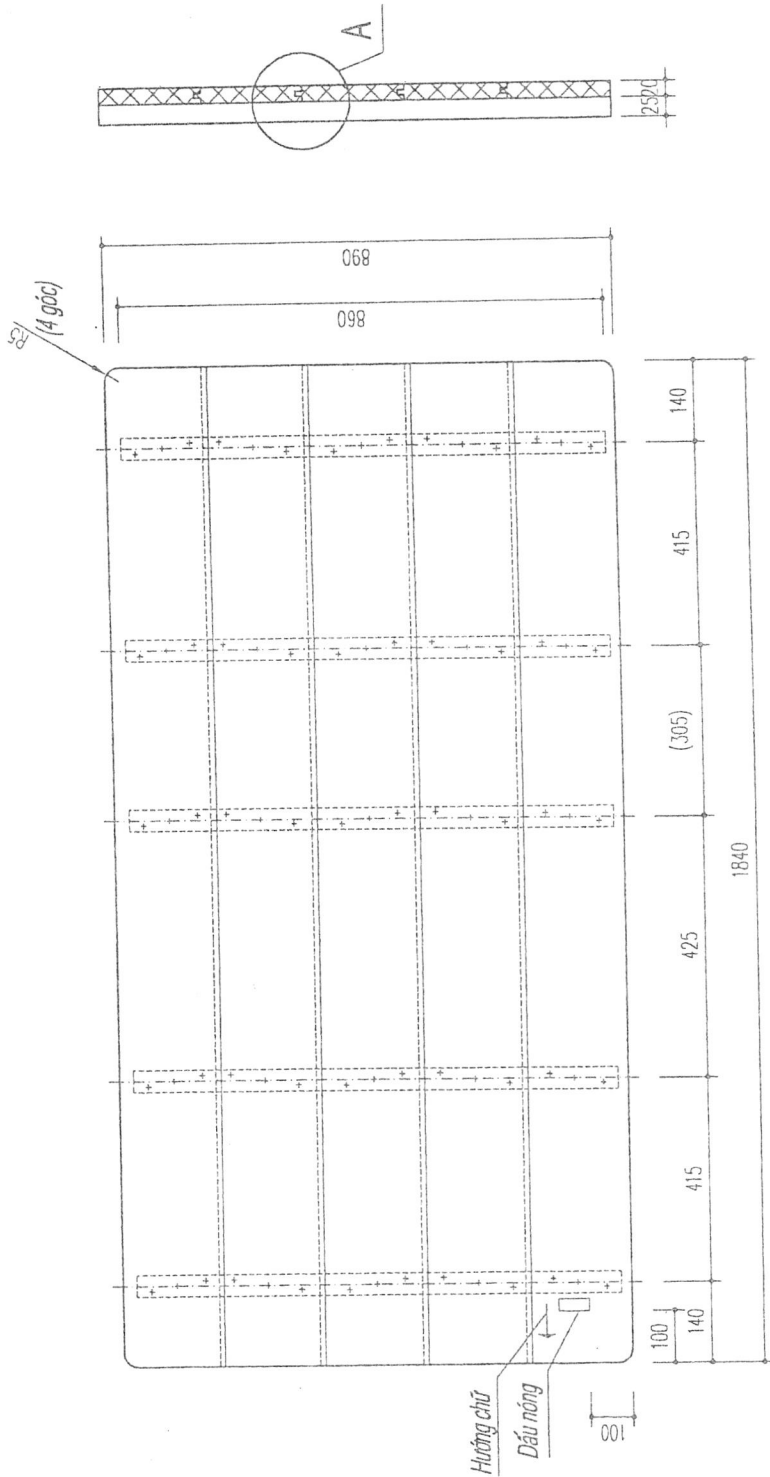

MỐI GHÉP A

TL 1:2

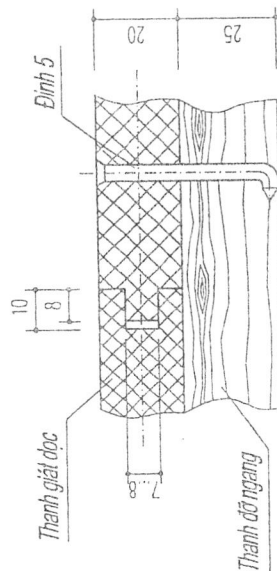

- Kích thước 1840x890x20mm dùng gỗ nhóm IV (ghép không quá 5 tấm; chiều ngang mỗi tấm ≥ 150 mm) được ngâm tẩm kỹ, sấy khô
- Dấu nong được đóng chìm vào góc phản. Kích thước 65x35mm; ghi rõ tháng năm và đơn vị sản xuất